


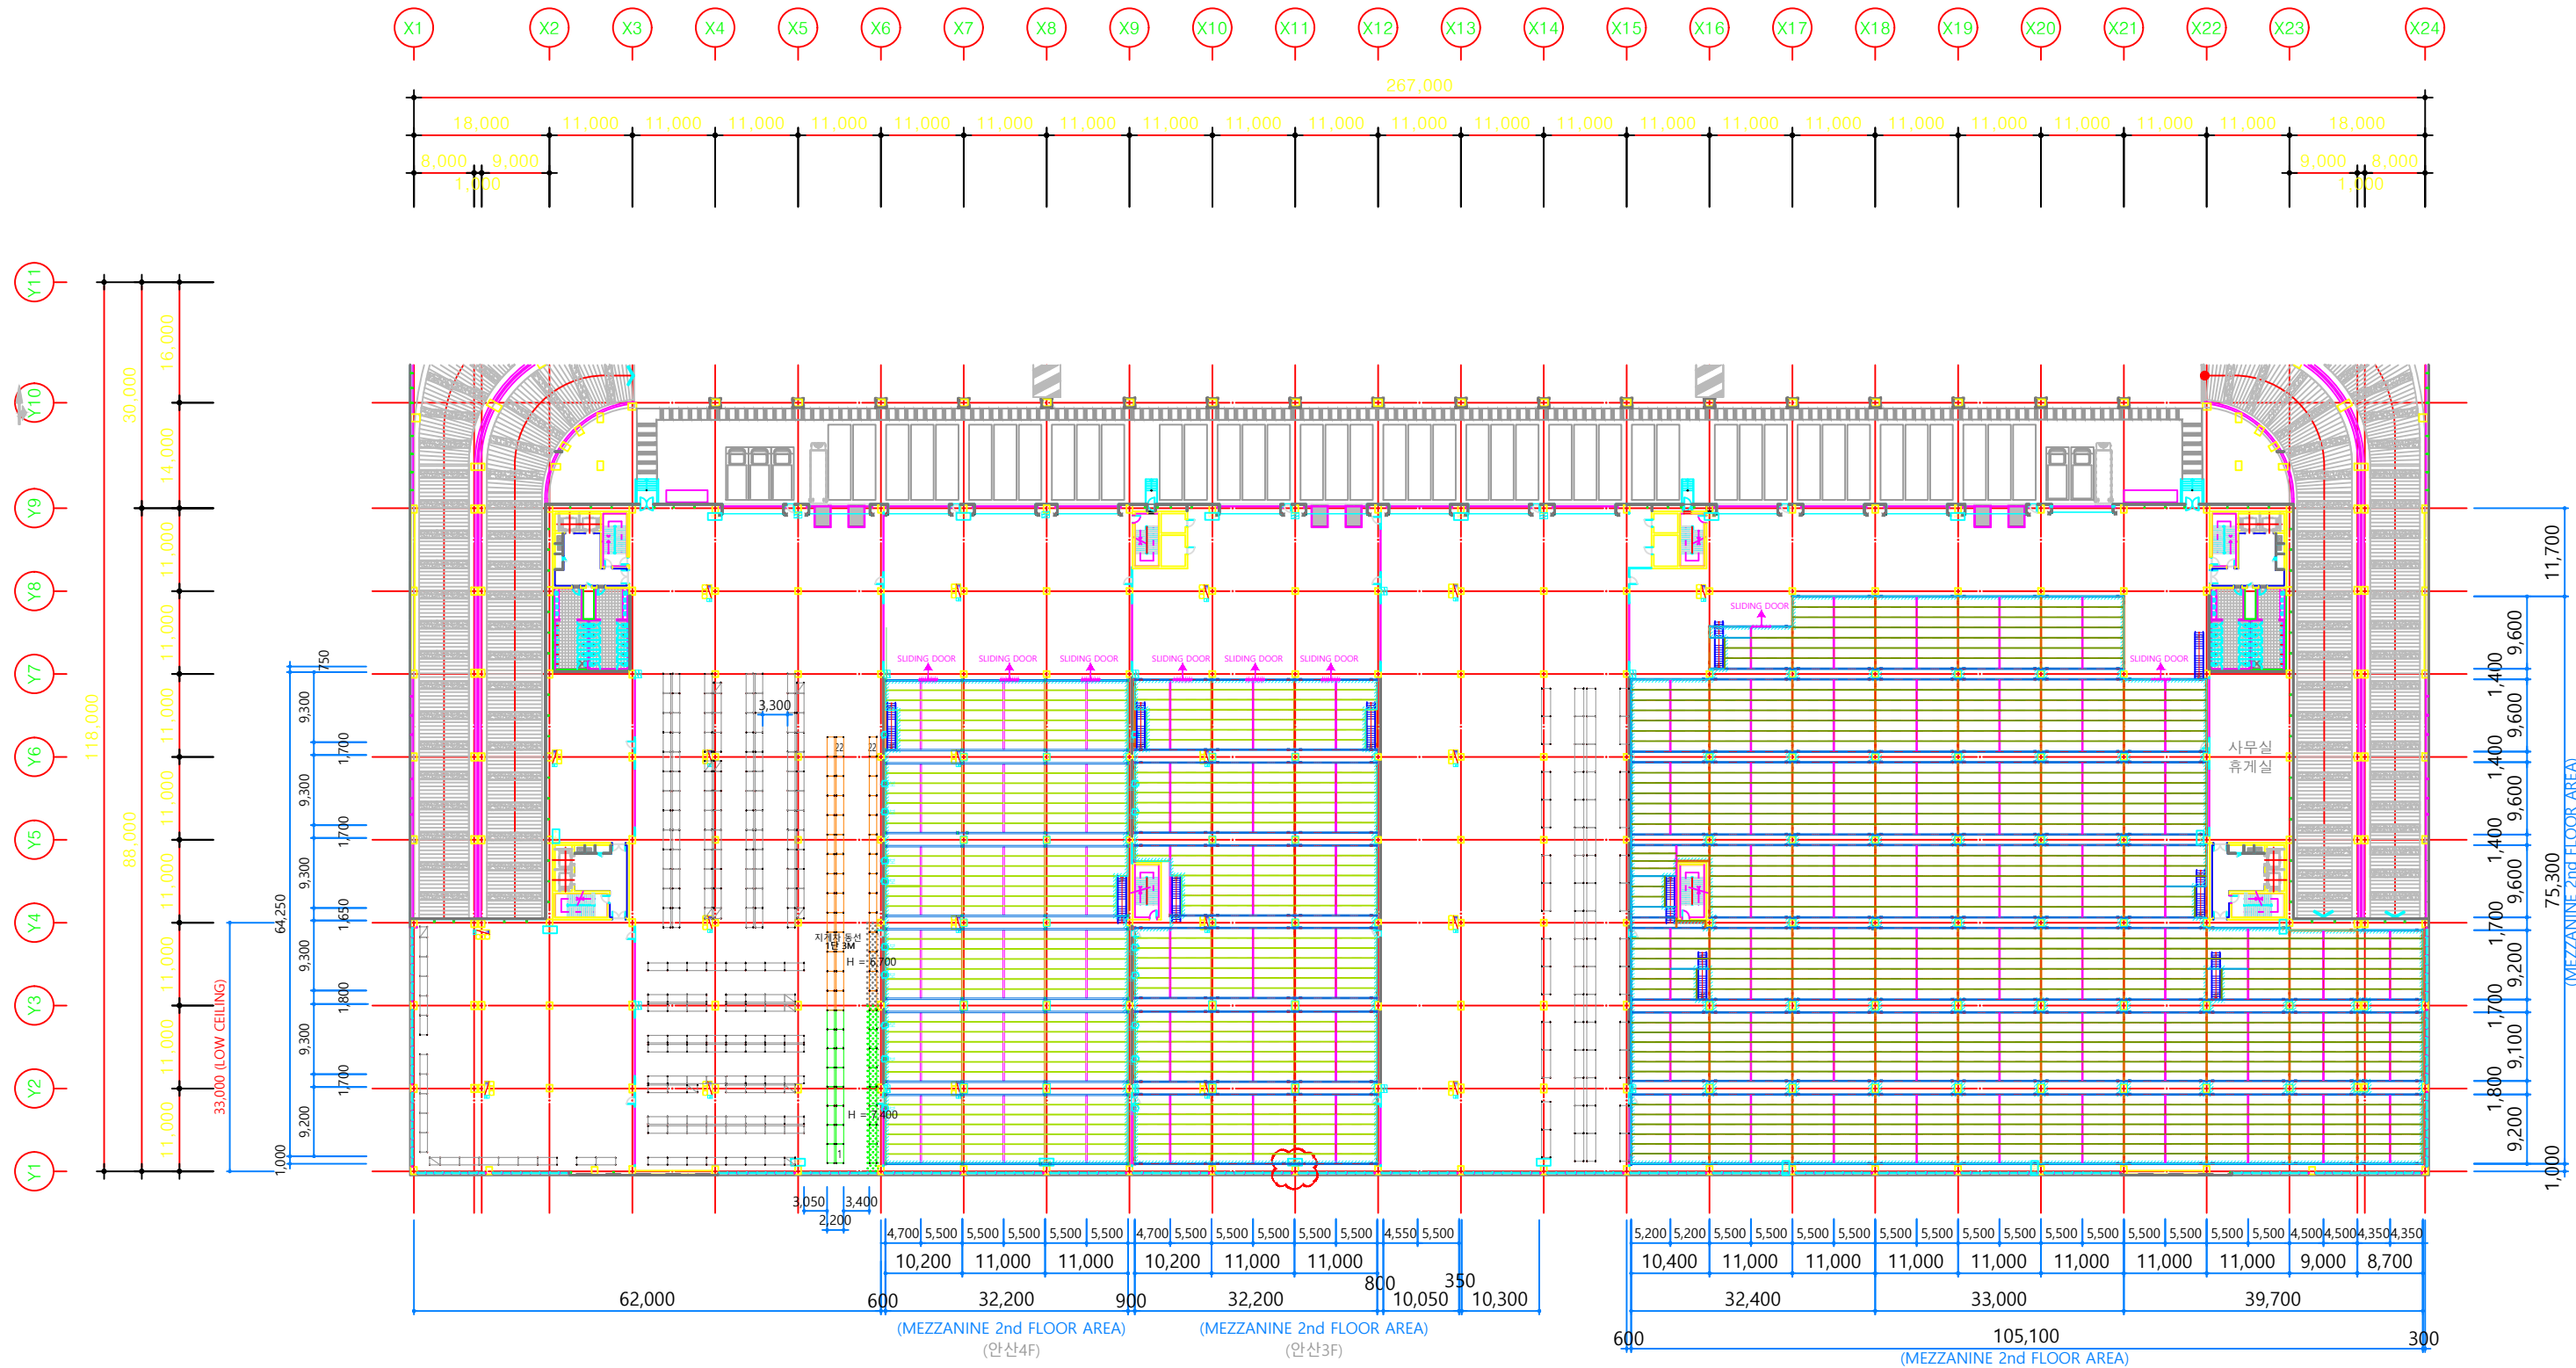

*** NOTE ***

			TYPE	RACK SIZE		QT'Y	STEP	PLT/STEP	LOAD CAPA.				REMARK				
1	MEZZANINE FLOOR 1			(W)32,200*(D)64,200*(H)4,040		1 SET	2 Floor	2nd floor	32.2m*64.2m = 2,068m² = 626PY								
2	POST 1(SS275)			H - 200*200*8t*12t													
3																	
4	PALLET RACK(기존자재)			(W)2,535*(D)1,000*(H)6,000		24 SET	4 STEP	2 PLT/STEP	2 PLT * 4 STEP * 24 RACK = 192 PALLET LOAD								
5	PALLET RACK(추가자재)			(W)2,535*(D)1,000*(H)6,300		42 SET	4 STEP	2 PLT/STEP	2 PLT * 4 STEP * 42 RACK = 336 PALLET LOAD								
6									TOTAL = 528 PALLET LOAD								
7	MAIN BEAM 1			H-500*200*10T*16T		9	SUB. BEAM 1			H-450*200*9T*14T		10	CROSS BEAM 1			H-200*100*5.5T*8T	
8	MAIN BEAM 2			H-450*200*9T*14T													

5-01

WAREHOUSE 2F TOTAL RACK LAY OUT

(2-2F MEZZANINE BEAM LAYOUT)

ITEM	PART NO.	QTY	DESCRIPTION
TITLE	2F RACK SYSTEM LAY-OUT(아암2F원다)		OWNER NAME
DRAWING NO.	ICP24SLKAAM05-LA001		CHK'D Choi d h(10/08 '24)
DATE	2024.10.08.	SCALE	1/900
		DRAWN	Kim W S



주식회사 아아씨퍼로지템
In Cheon Precision Logistics System. CO., LTD.