


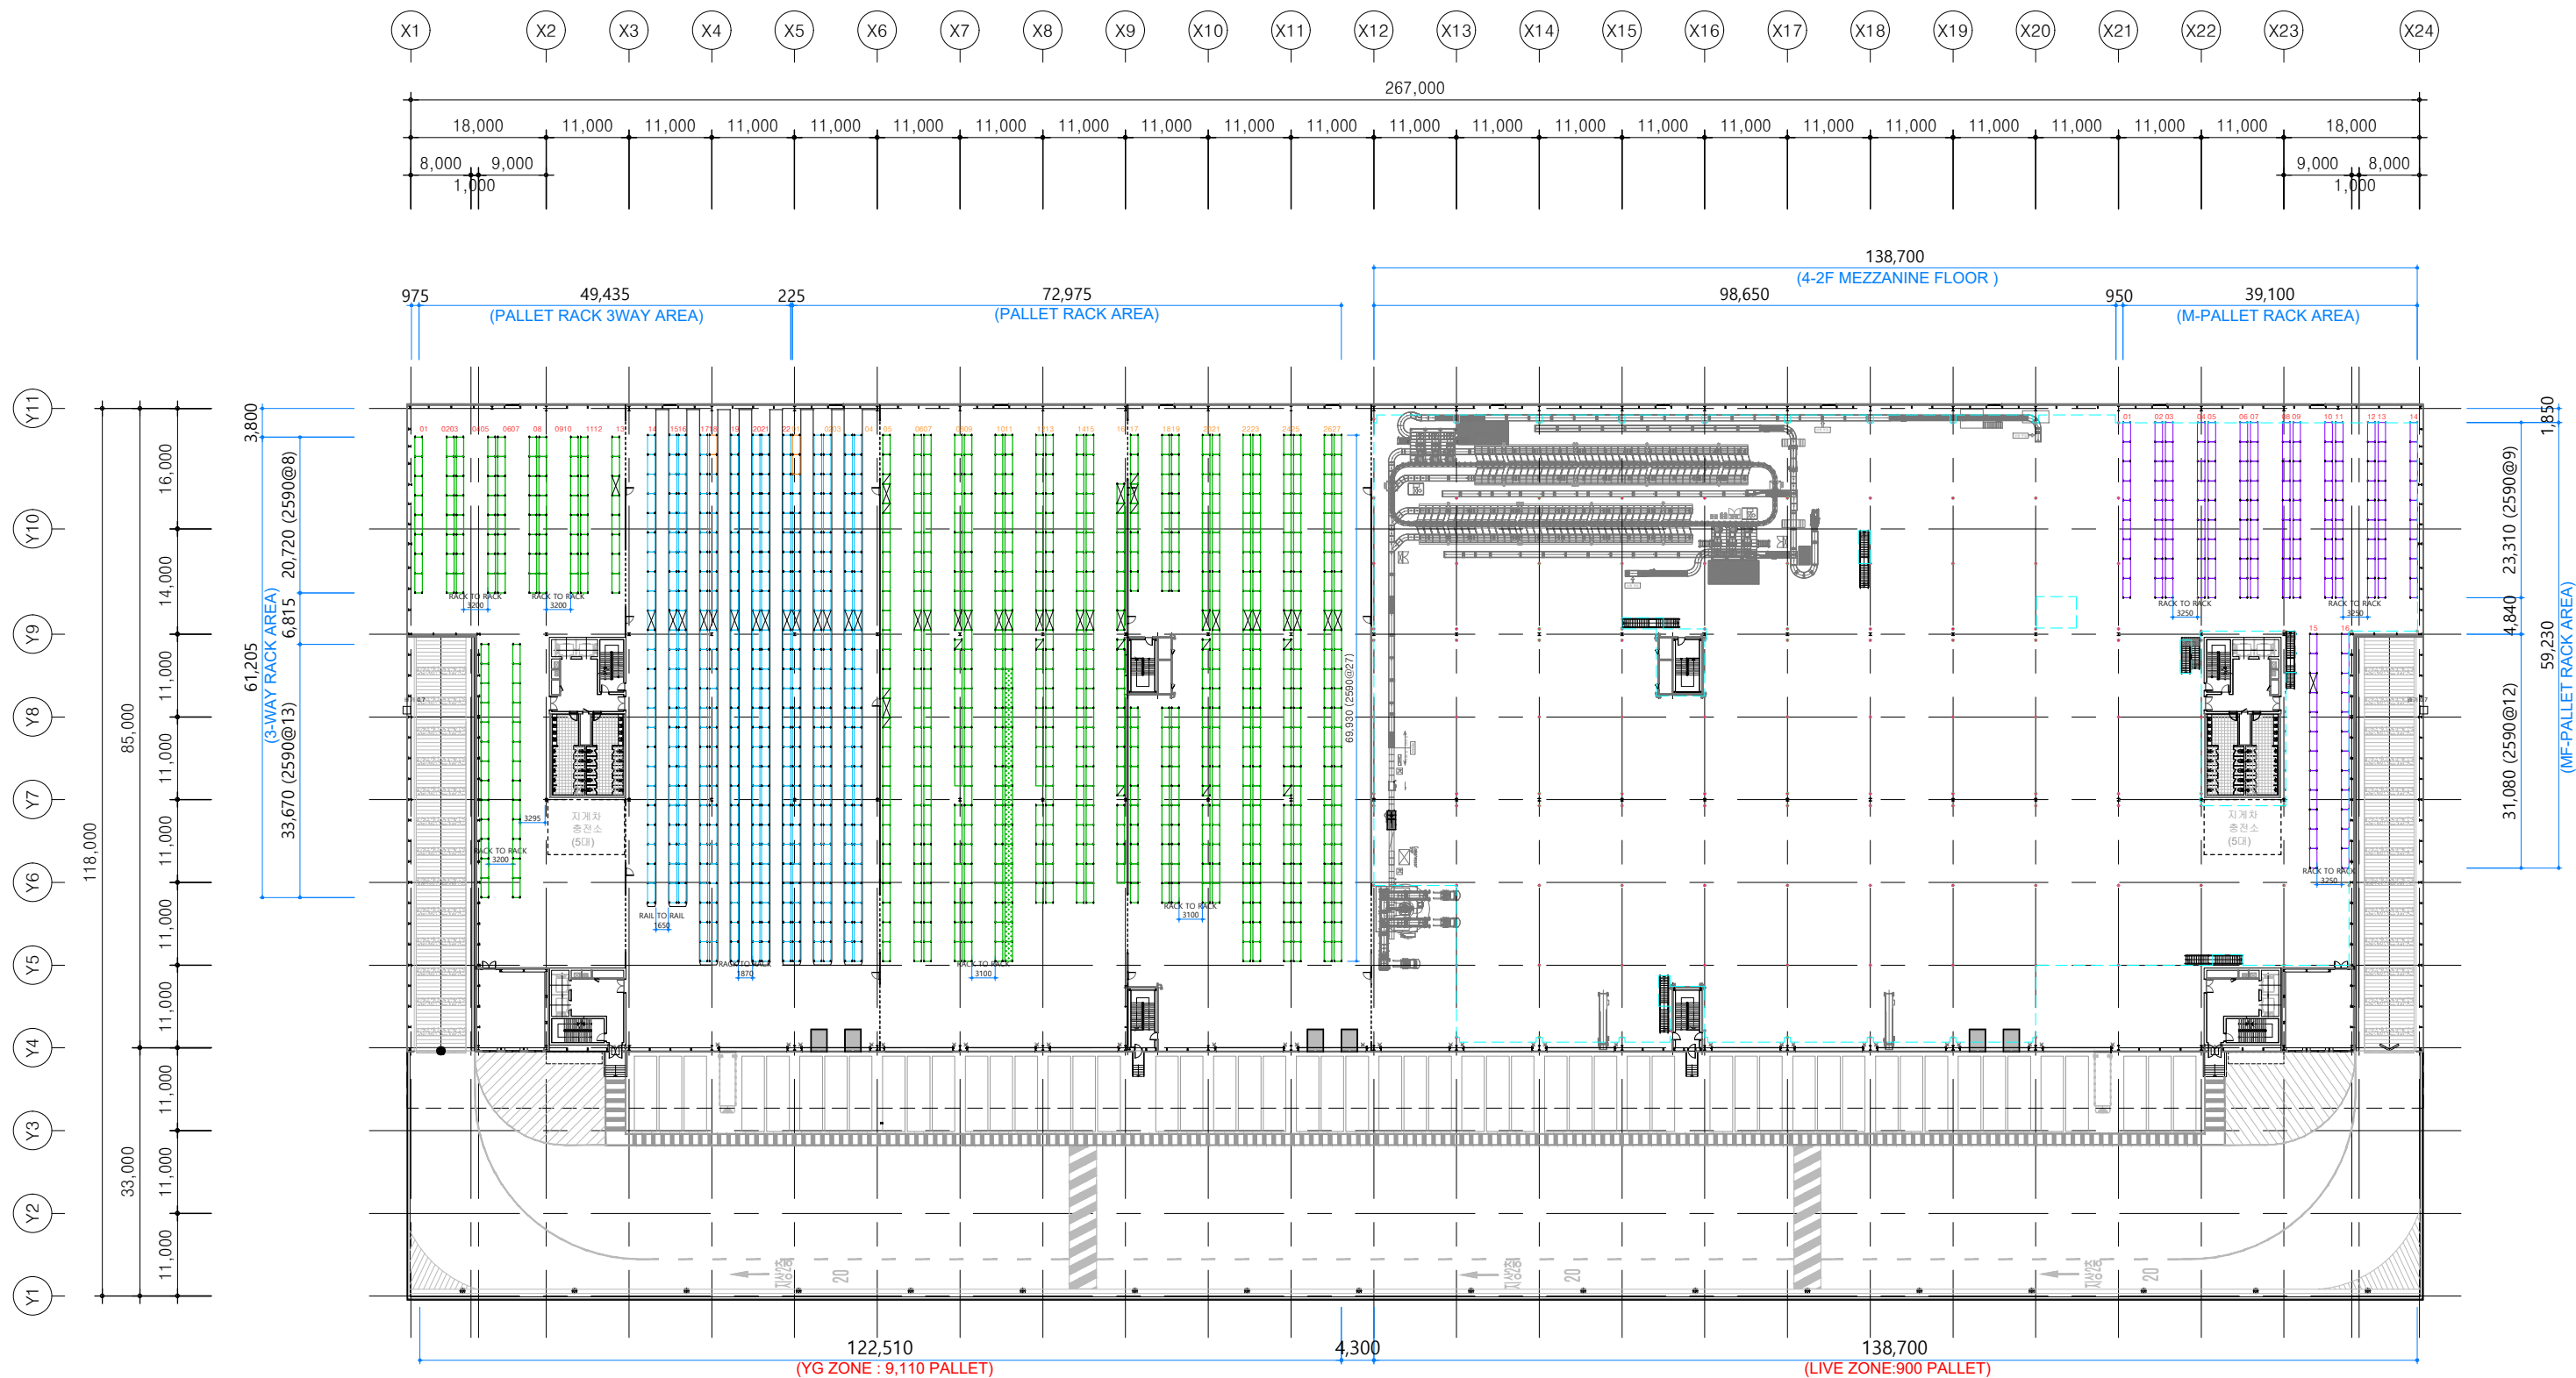

※ KS T 2027에 의거한 단열형 랙 / 복열형 랙 / 가이드 레일식 랙
- 강판 : KS D 3501, KS D 3503, KS D 3512, KS D 3519 이와 동등 이상의 것 적용.
- 강관 : KS D 3507, KS D 3517, KS D 3566, KS D 3568 이와 동등 이상의 것 적용.
- 연결부재 : KS B 1002, KS B 1012 이와 동등 이상의 것 적용.

*** NOTE ***

NO.	RACK NAME	TYPE	RACK SIZE	QT'Y	STEP	PLT/STEP	LOAD CAPA.	REMARK
1	PALLET RACK 1(3WAY)		(W)2,590*(D)1,000*(H)8,900	375 SET	5 STEP	2 PLT/STEP	2 PLT * 5 STEP * 375 RACK = 3,750 PALLET LOAD	TOTAL : 3,852 PALLET LOAD
2	PALLET RACK 2(3WAY)		(W)2,590*(D)1,000(H)8,900<통로>	9 SET	3 STEP	2 PLT/STEP	2 PLT * 3 STEP * 9 RACK = 54 PALLET LOAD	
3	PALLET RACK 3(3WAY)		(W)2,590*(D)1,000*(H)6,800	6 SET	4 STEP	2 PLT/STEP	2 PLT * 4 STEP * 6 RACK = 48 PALLET LOAD	
4	PALLET RACK 1		(W)2,590*(D)1,000*(H)6,600	620 SET	4 STEP	2 PLT/STEP	2 PLT * 4 STEP * 620 RACK = 4,960 PALLET LOAD	TOTAL : 5,258 PALLET LOAD
5	PALLET RACK 2		(W)2,590*(D)1,000(H)6,600<통로>	28 SET	2 STEP	2 PLT/STEP	2 PLT * 2 STEP * 28 RACK = 112 PALLET LOAD	
6	PALLET RACK 3		(W)1,295*(D)1,000(H)6,600	24 SET	4 STEP	1 PLT/STEP	1 PLT * 4 STEP * 24 RACK = 96 PALLET LOAD	
6	PALLET RACK 4		(W)2,590*(D)1,000*(H)6,600<선반추가>	15 SET	3 STEP	2 PLT/STEP	2 PLT * 3 STEP * 15 RACK = 90 PALLET LOAD	TOTAL : 896 PALLET LOAD
7	PALLET RACK 1(M-LITCH)		(W)2,590*(D)1,000*(H)4,900	149 SET	3 STEP	2 PLT/STEP	2 PLT * 3 STEP * 149 RACK = 894 PALLET LOAD	
8	PALLET RACK 2(M-LITCH)		(W)2,590*(D)1,000*(H)4,900<통로>	1 SET	1 STEP	2 PLT/STEP	2 PLT * 1 STEP * 1 RACK = 2 PALLET LOAD	
9	MEZZANINE FLOOR1		(W)138,700*(D)83,400*(H)5,000	1 SET	4 Floor	2nd floor	138.7m*83.4m = 10,002m² = 3,026PY	

1-01

WAREHOUSE 4F TOTAL RACK LAY OUT

04

(4-1F PALLET RACK LAYOUT)

ITEM	PART NO.	Q'TY	DESCRIPTION	
TITLE	4F RACK SYSTEM LAY-OUT(아암물류센터)		OWNER NAME	
DRAWING NO.	ICP23AAM02-LA001		CHK'D	Choi d h(01/31 '24)
DATE	2024.01.31.		SCALE	1/900
			DRAWN	Shin S M

주식회사 아아씨피로지템
In Cheon Precision Logistics System. CO., LTD.